


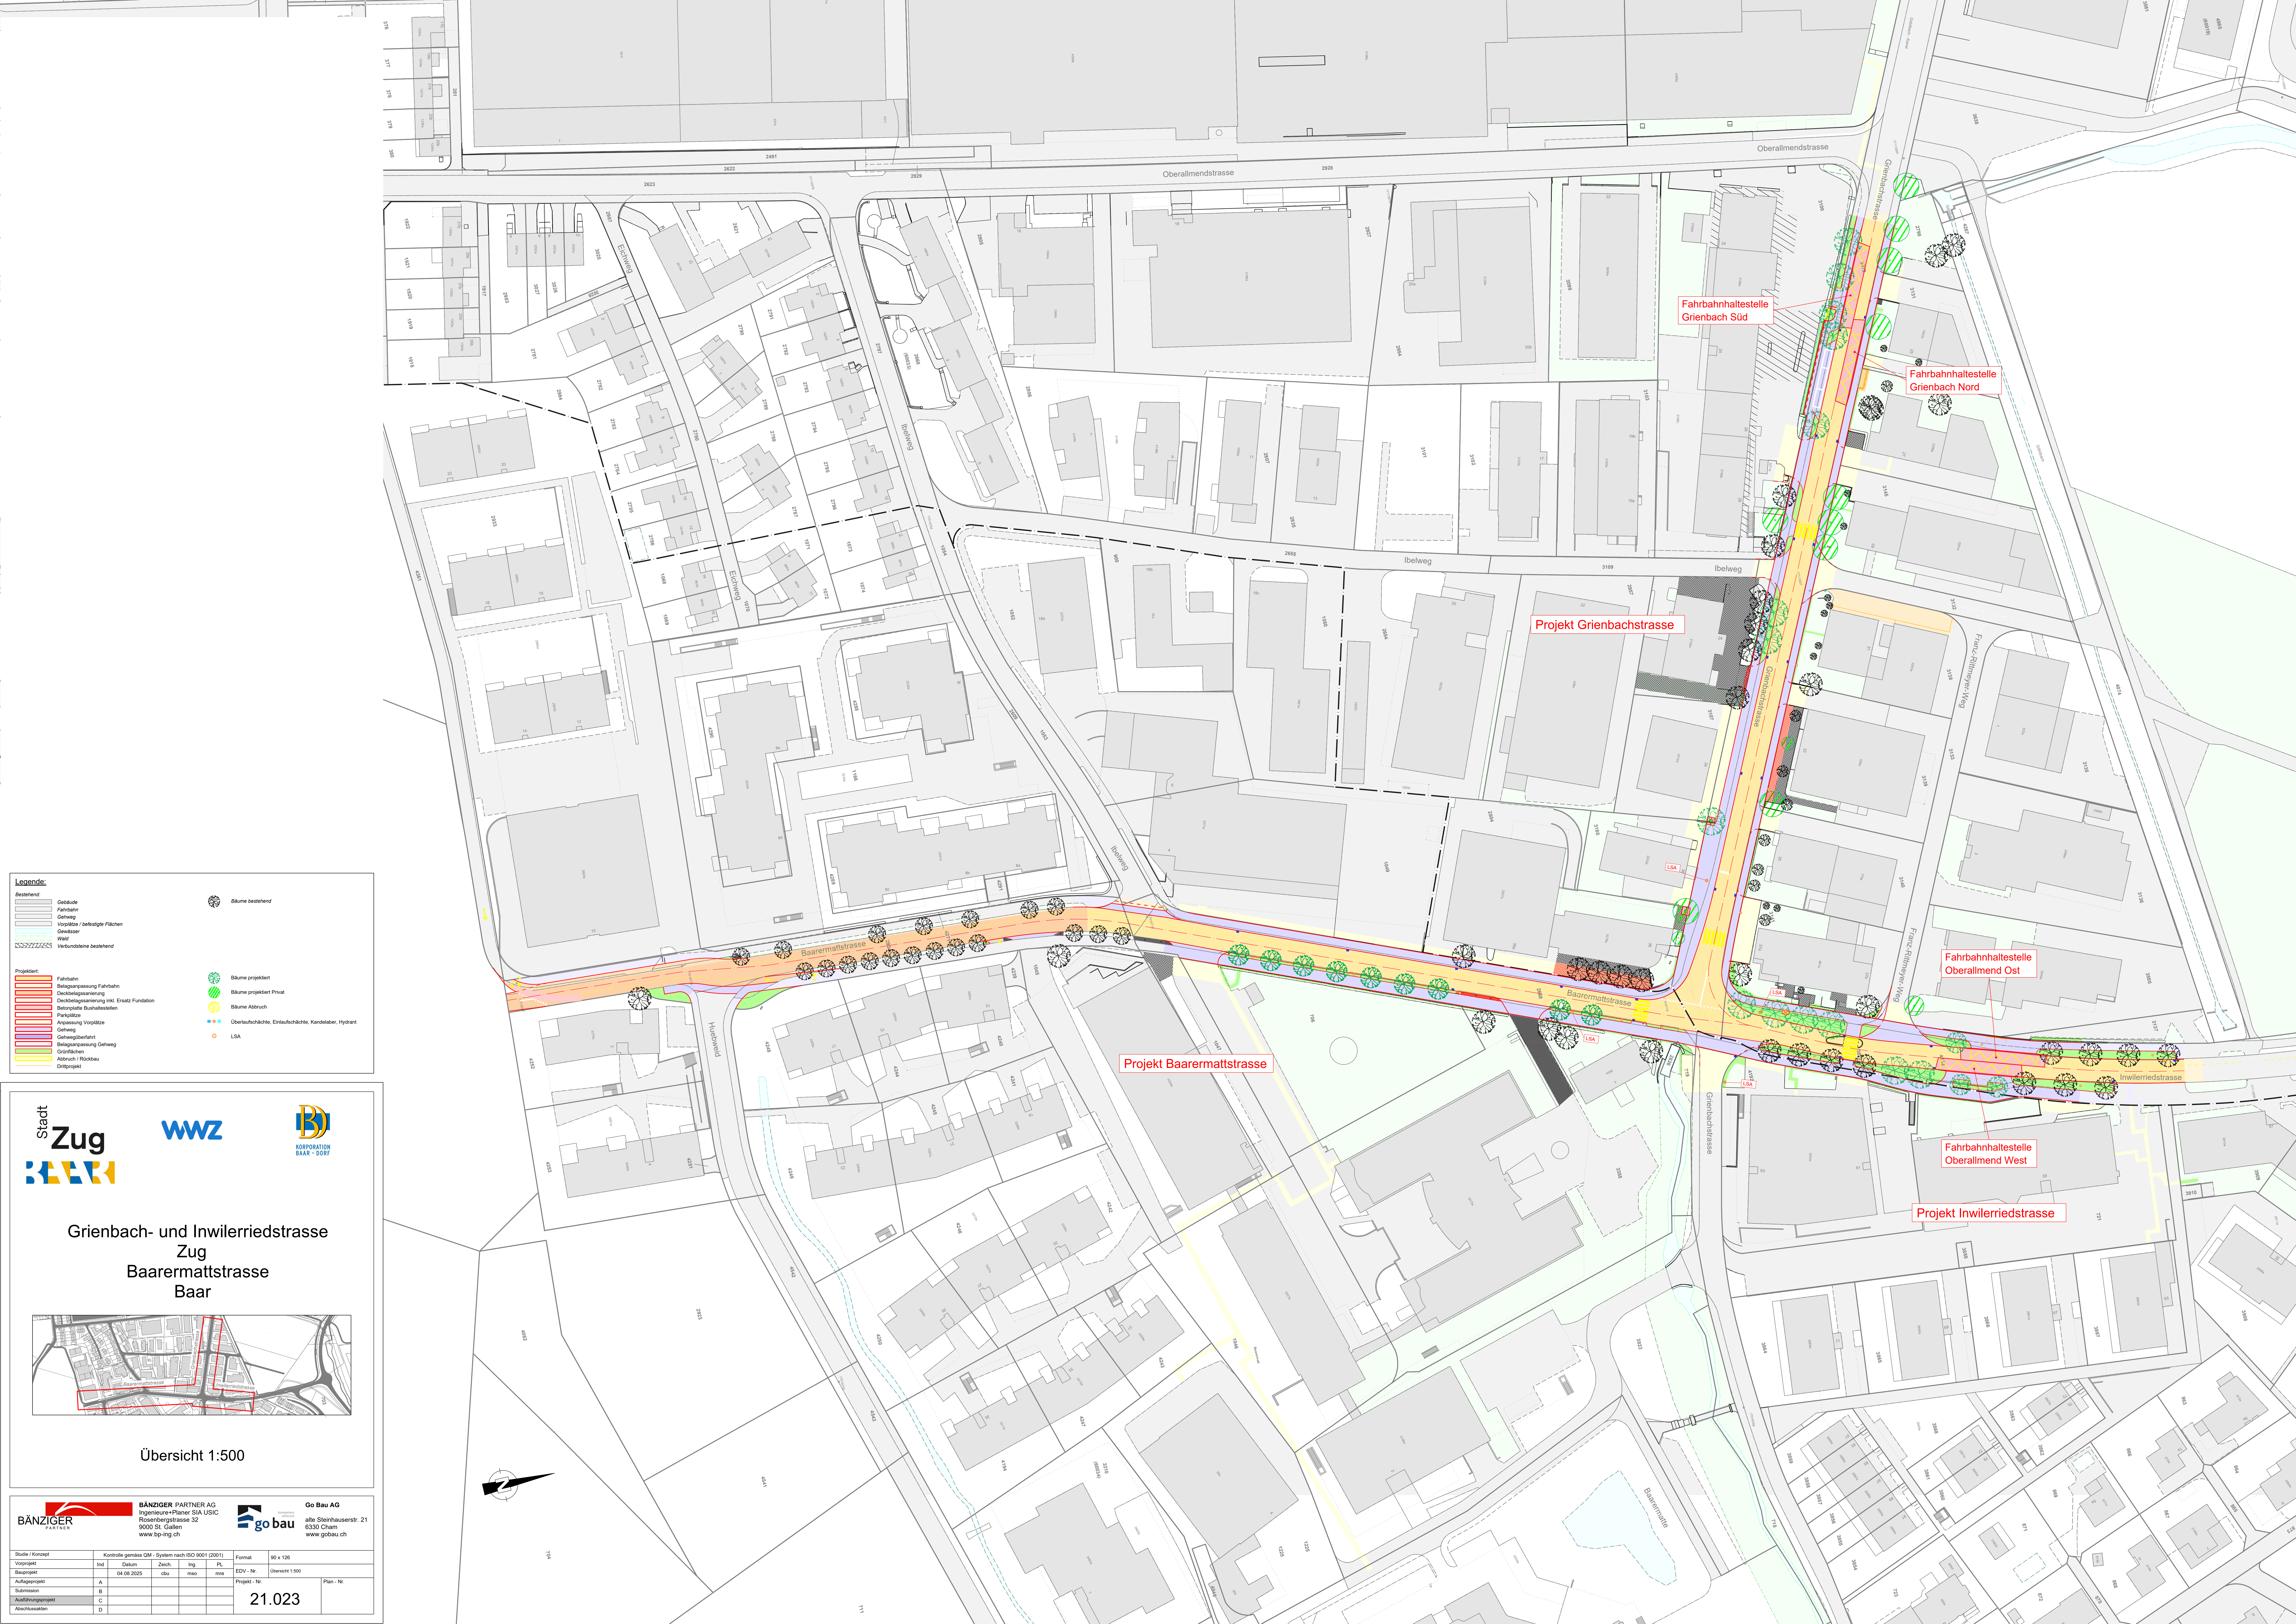

Legende:

Bestehend:

- Gebäude
- Festum
- Gehweg
- Vorplatz / befestigte Flächen
- Gelände
- Wald
- Vorunterste bestehend

Projekt:

- Fahrbahn
- Belagsplanung Fahrbahn
- Deckungsplanung
- Deckungsplanung inkl. Ersatz Fundament
- Belagplan Baustellen
- Parkplätze
- Abgrenzung Vorplatz
- Gehweg
- Gehwegüberlappung
- Belagsplanung Gehweg
- Grünflächen
- Abgrenzung / Rückbau
- Drittpunkt

Bäume:

- Bäume bestehend
- Bäume projektiert
- Bäume projektiert Privat
- Bäume Abgrenzung
- Überlappungsbäume, Einbaubäume, Kandelaber, Hydrant
- LSA

Stadt Zug

WWZ

KORPORATION BAAR - ZUG

Grienbach- und Inwilerriedstrasse
Zug
Baarermattstrasse
Baar

Übersicht 1:500

BÄNZIGER PARTNER AG

Ingenieur-Planer SIA USIG

Rosenbergstrasse 32

8000 St. Gallen

www.banziger.ch

go bau

alle Steinhäuserstr. 21

6300 Cham

www.gobau.ch

Stufe / Konzept	Kontrolle gemäss QM-System nach ISO 9001 (2001)	Format	90 x 120
Vorprojekt	Entwurf	EDV- Nr.	Übersicht 1:500
Entwurf	04.08.2025	ing	
Auftraggeber	A	ing	
Entwurf	B	ing	
Entwurf	C	ing	
Entwurf	D	ing	

11.023

Plan- Nr.

